



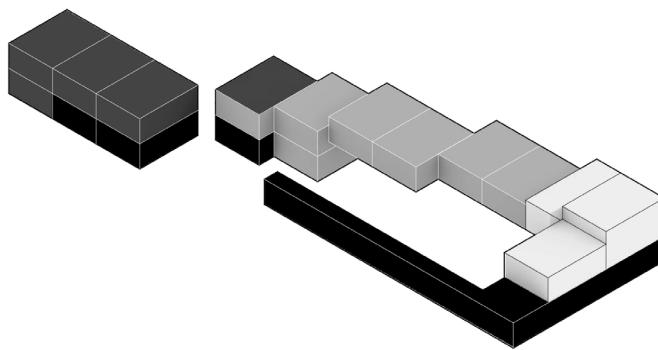


ZAIHENG LIANG

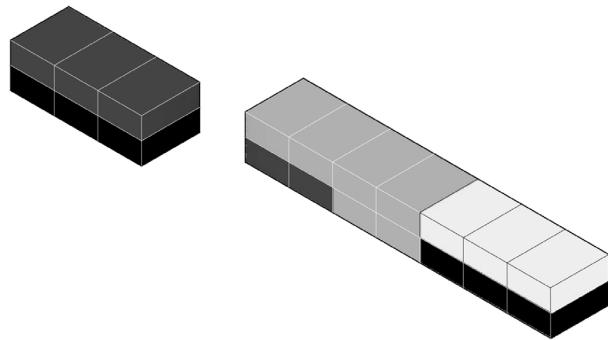

REARRANGEMENT


- 3
- 2
- 1
- X

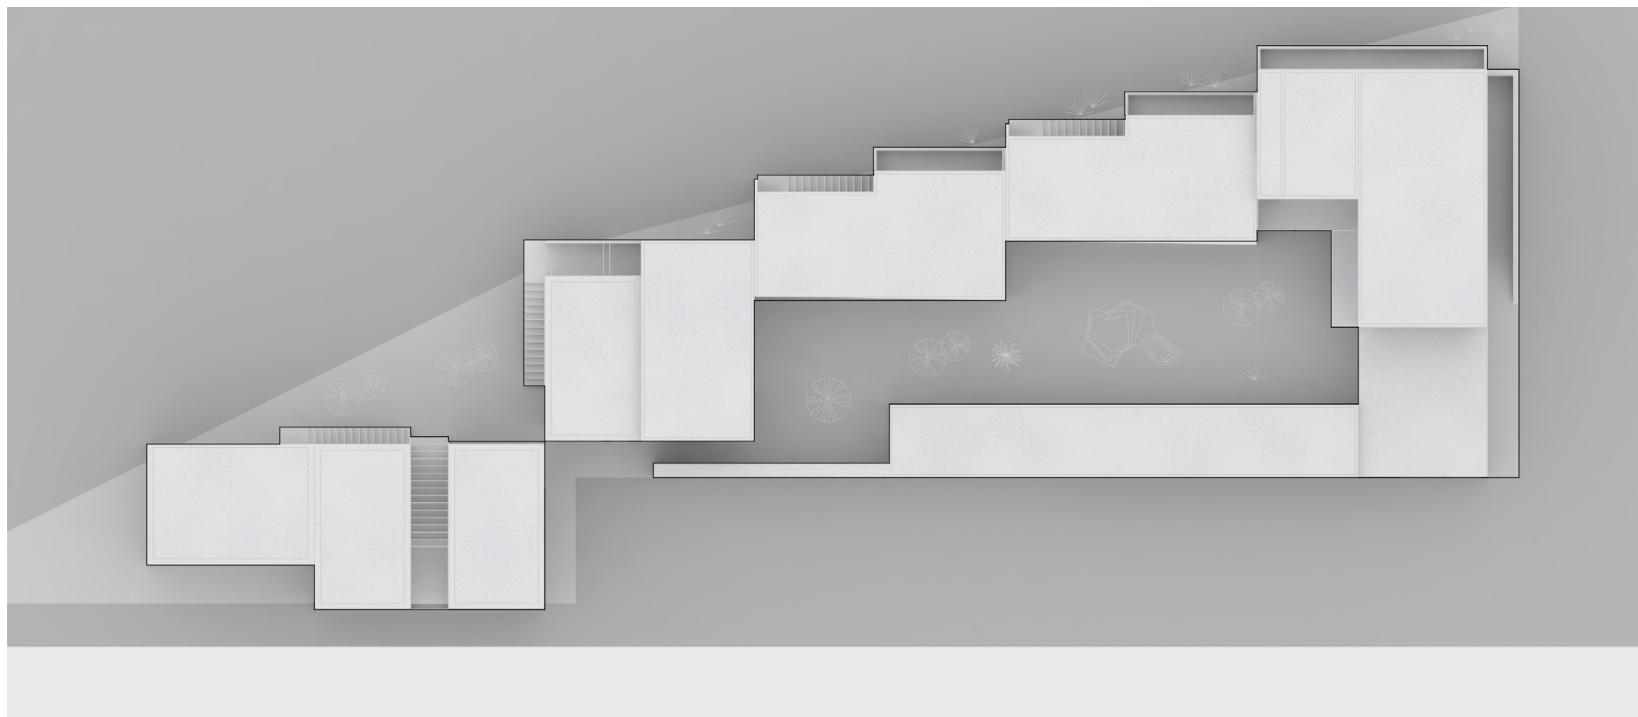


PLAN




SECTION

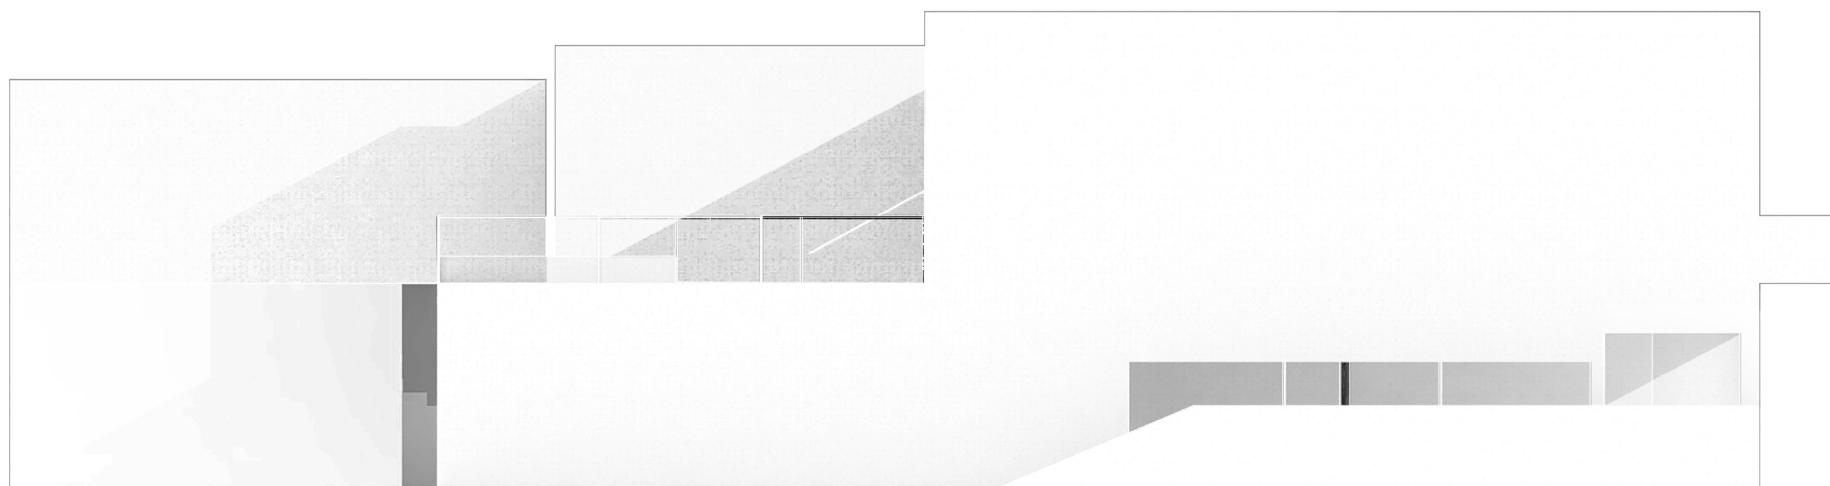


WEST

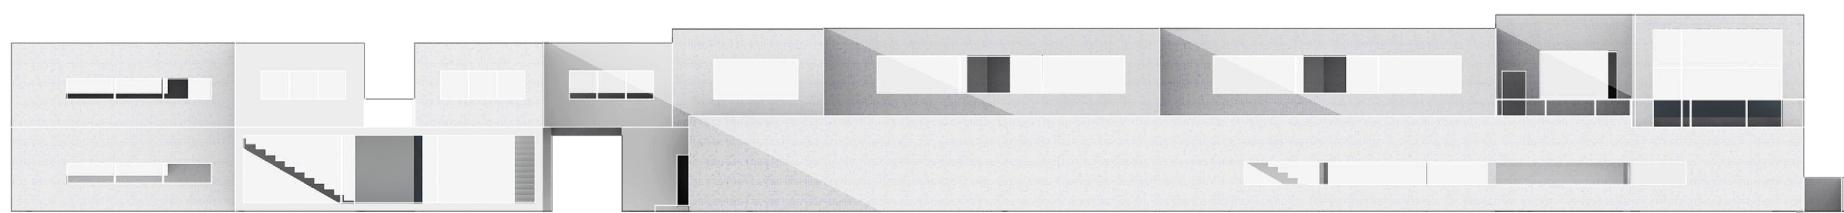


NORTH

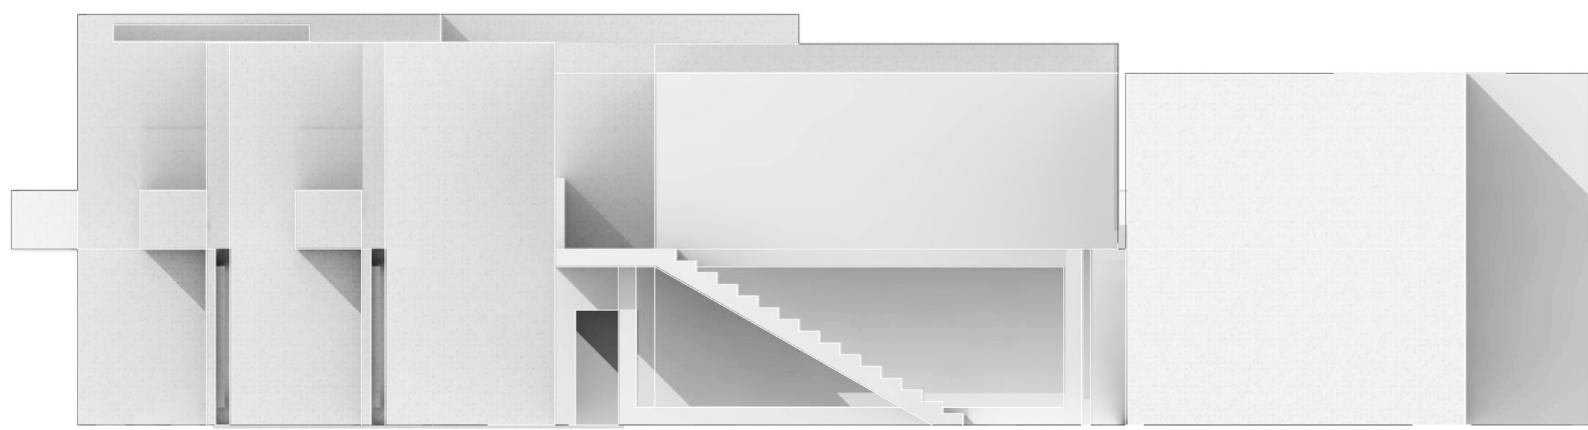

EAST

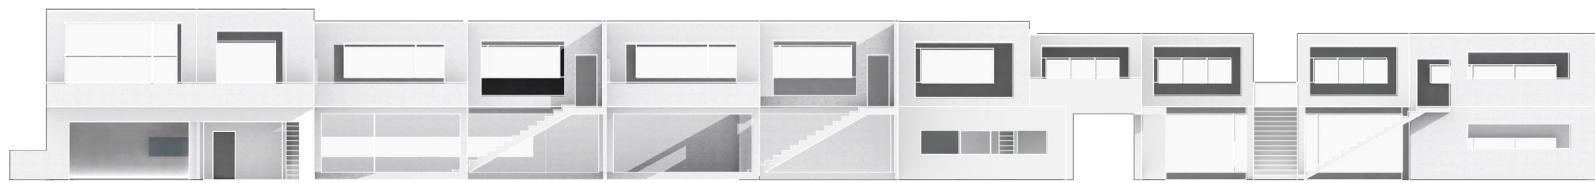


SOUTH

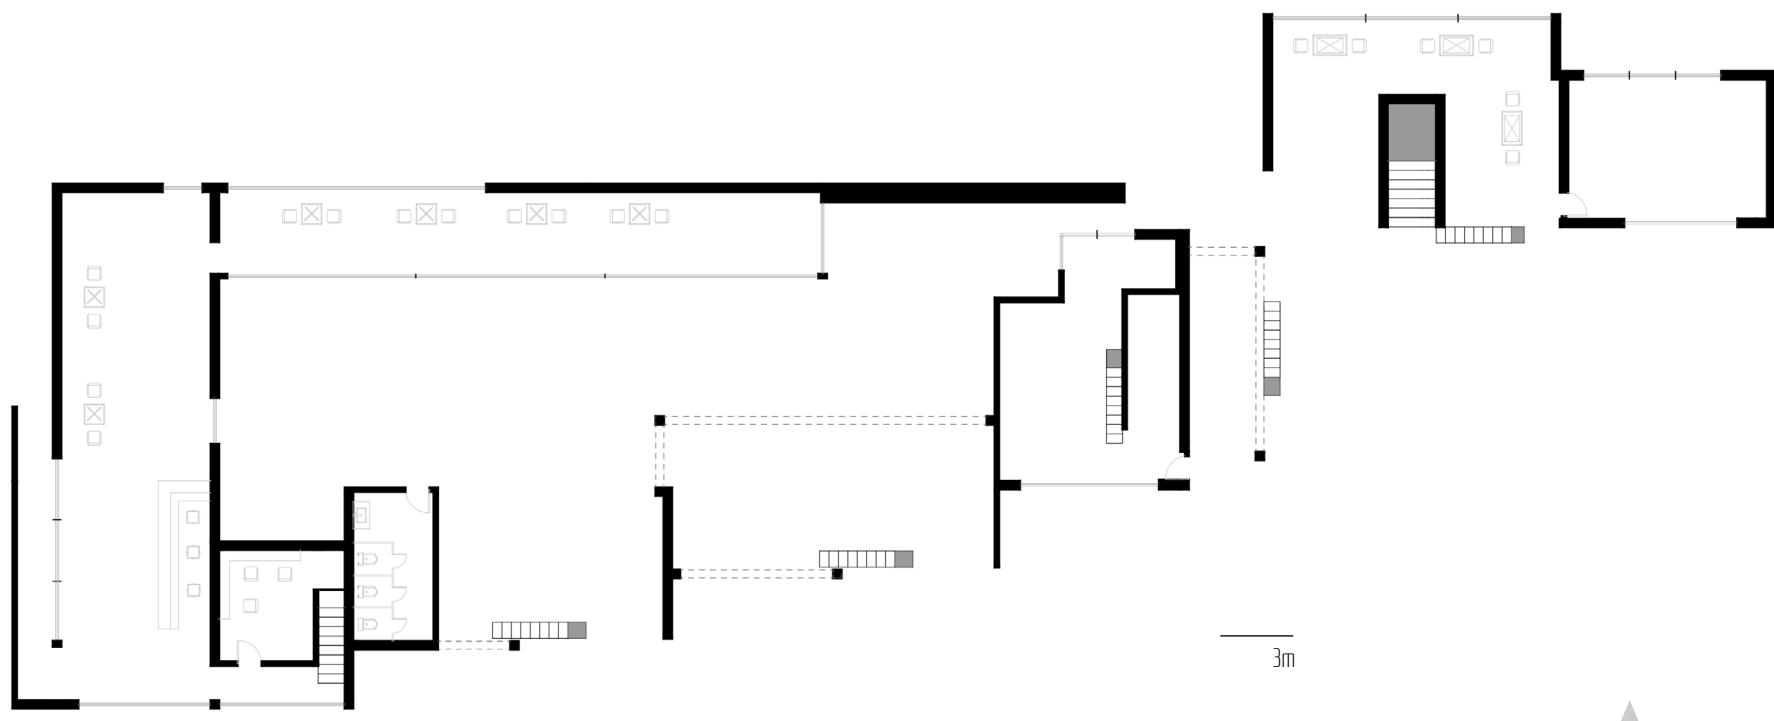

1ST FLOOR

N

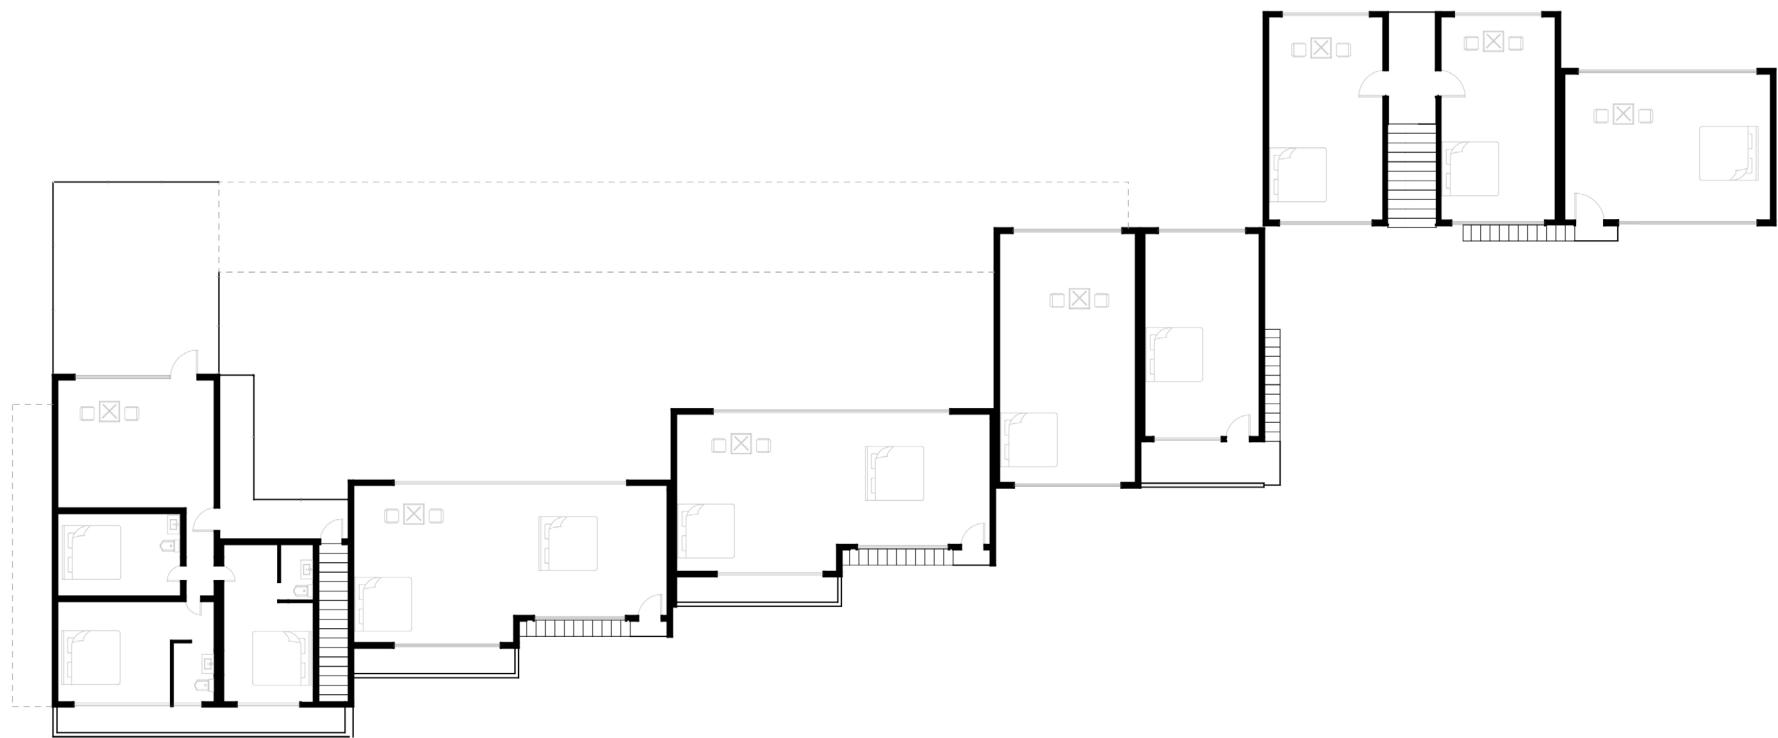

2ND FLOOR

